


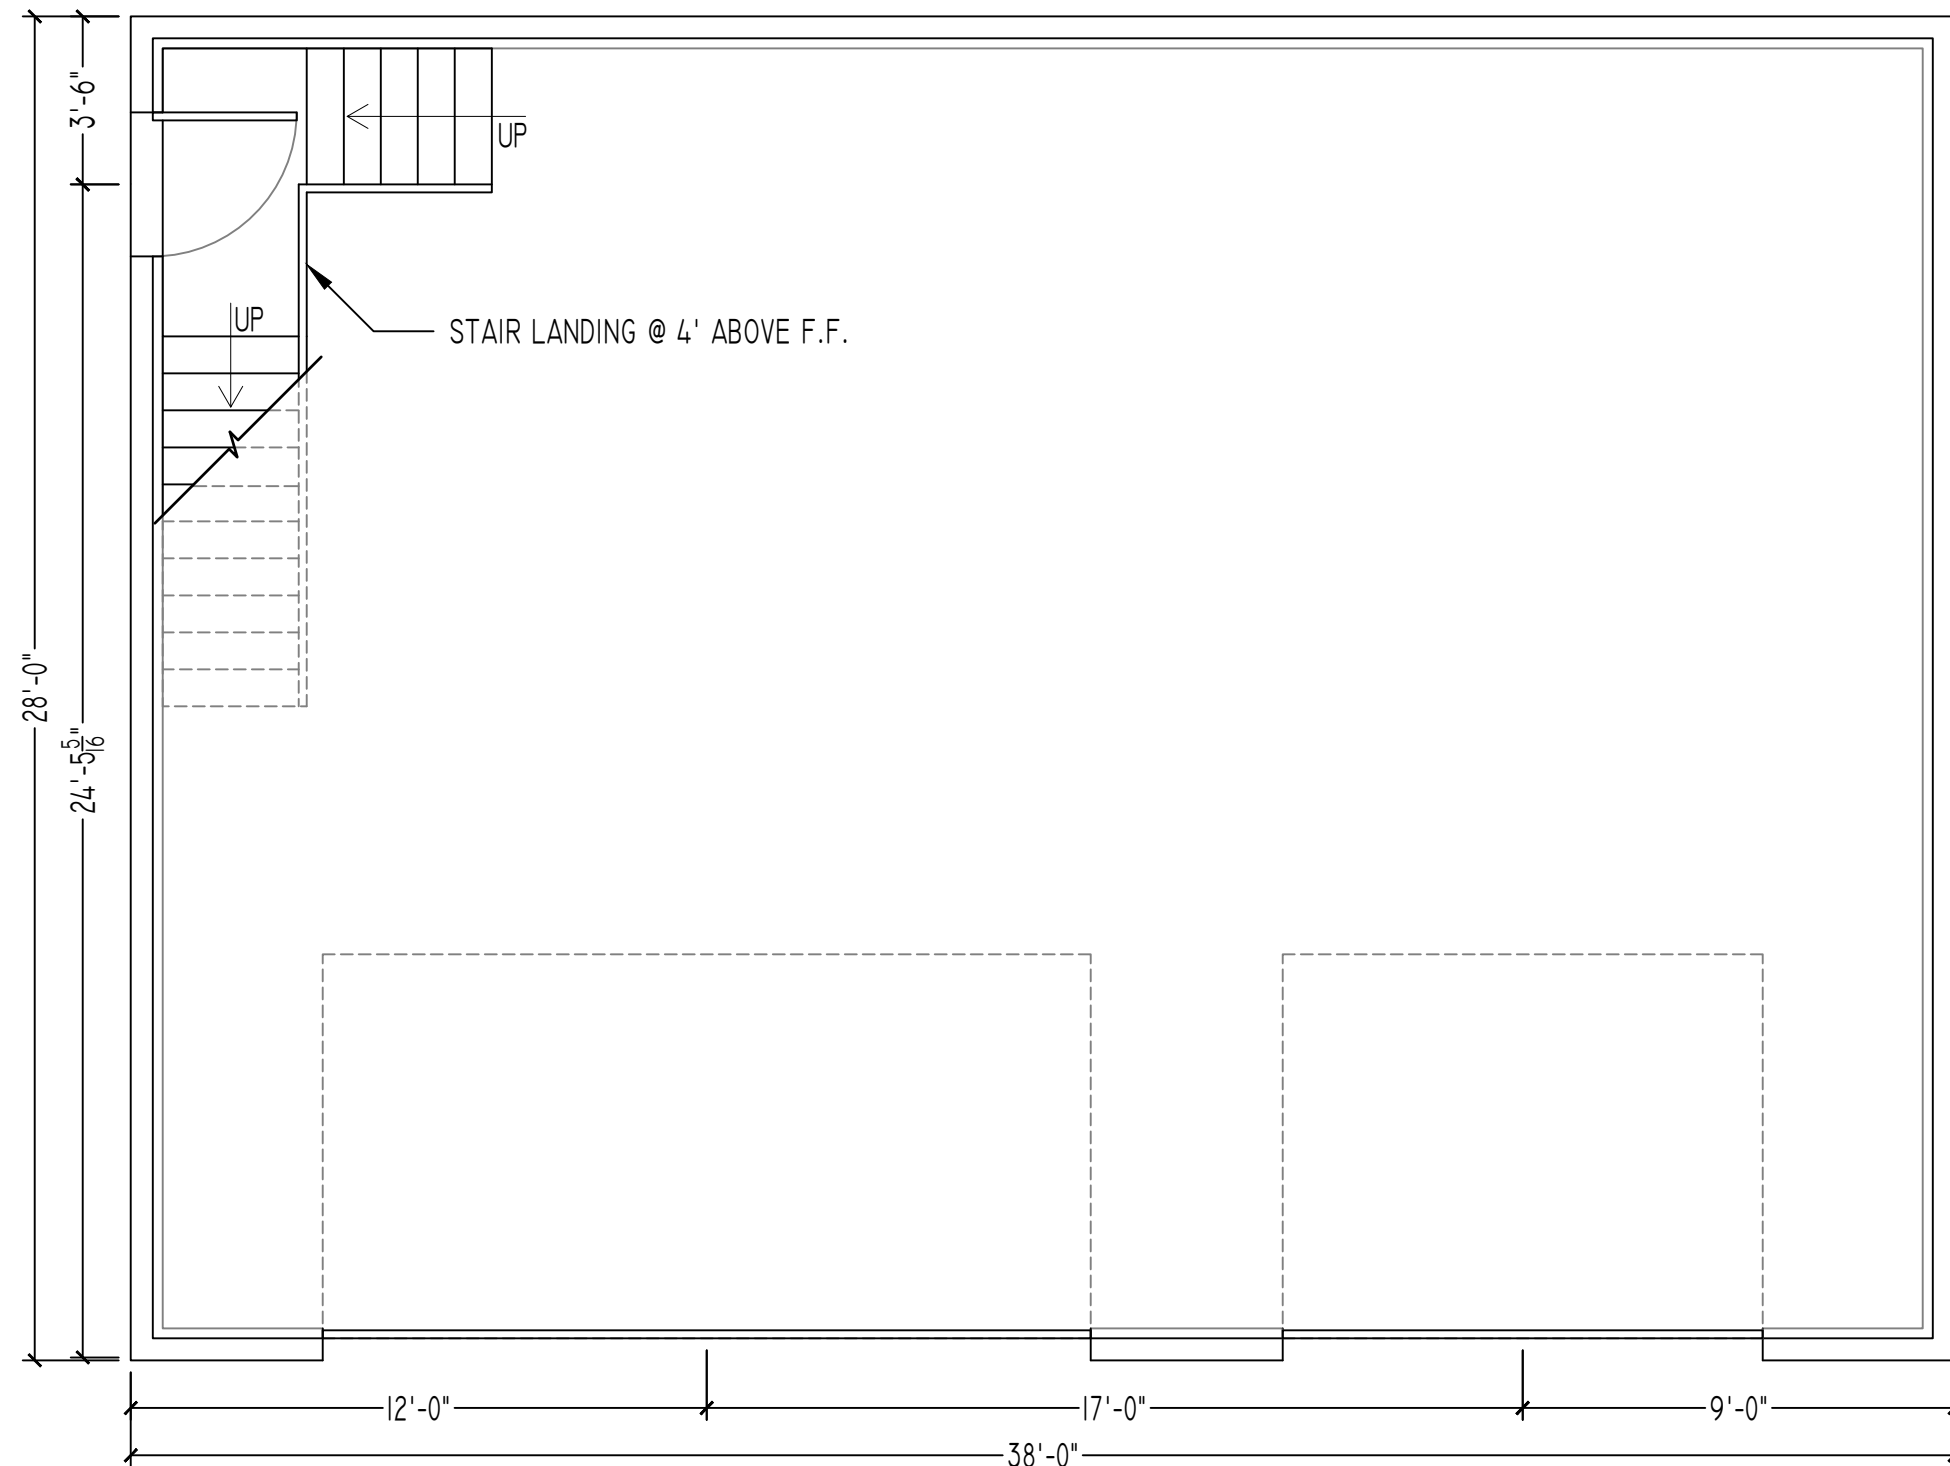

NOTES:

1. WALLS: 2" X 6" FRAMING, 7'-9" OR 9'-9" HIGH (VARIES)
2. SIDING: VINYL LOG SIDING / MIRATEC TRIM, BROWN
3. ROOFING: ASPHALT ARCHITECTURAL SHINGLES, BARKWOOD
4. DOORS: (1) 16' X 8' OVERHEAD DOOR, RANCH PANELS, WINDOWS, COCOA HICKORY PLANK
(1) 10' X 8' OVERHEAD DOOR, RANCH PANELS, WINDOWS, COCOA HICKORY PLANK
(1) 3' 9-LITE PRE-HUNG ENTRY DOOR, BRONZE
5. WINDOWS: (8) 36" X 48" ANDERSEN 400 SERIES DOUBLE HUNG WINDOWS, TERRATONE
(1) 30" X 36" ANDERSEN 400 SERIES DOUBLE HUNG WINDOWS, TERRATONE
6. CONCRETE: 6' POURED FROST WALL, 8" THICK ON 16" X 8" POURED FOOTINGS
4" POURED CONCRETE SLAB

FIRST FLOOR

CUSTOMER APPROVAL: _____
INITIALS DATE

TOWN OF FREMONT - SULLIVAN COUNTY - SBL#: 8-I-28.4			
BRIAN PIERCE 157 CROWLEY RD ROSCOE, NY 12776 201-783-2460		DATE DRAWN: MAY 2026	SHEET A-102
		SCALE: NOT TO SCALE	
		DRAWN BY: MIKE CAREY	
		LAST UPDATE: 6.5.2026	